


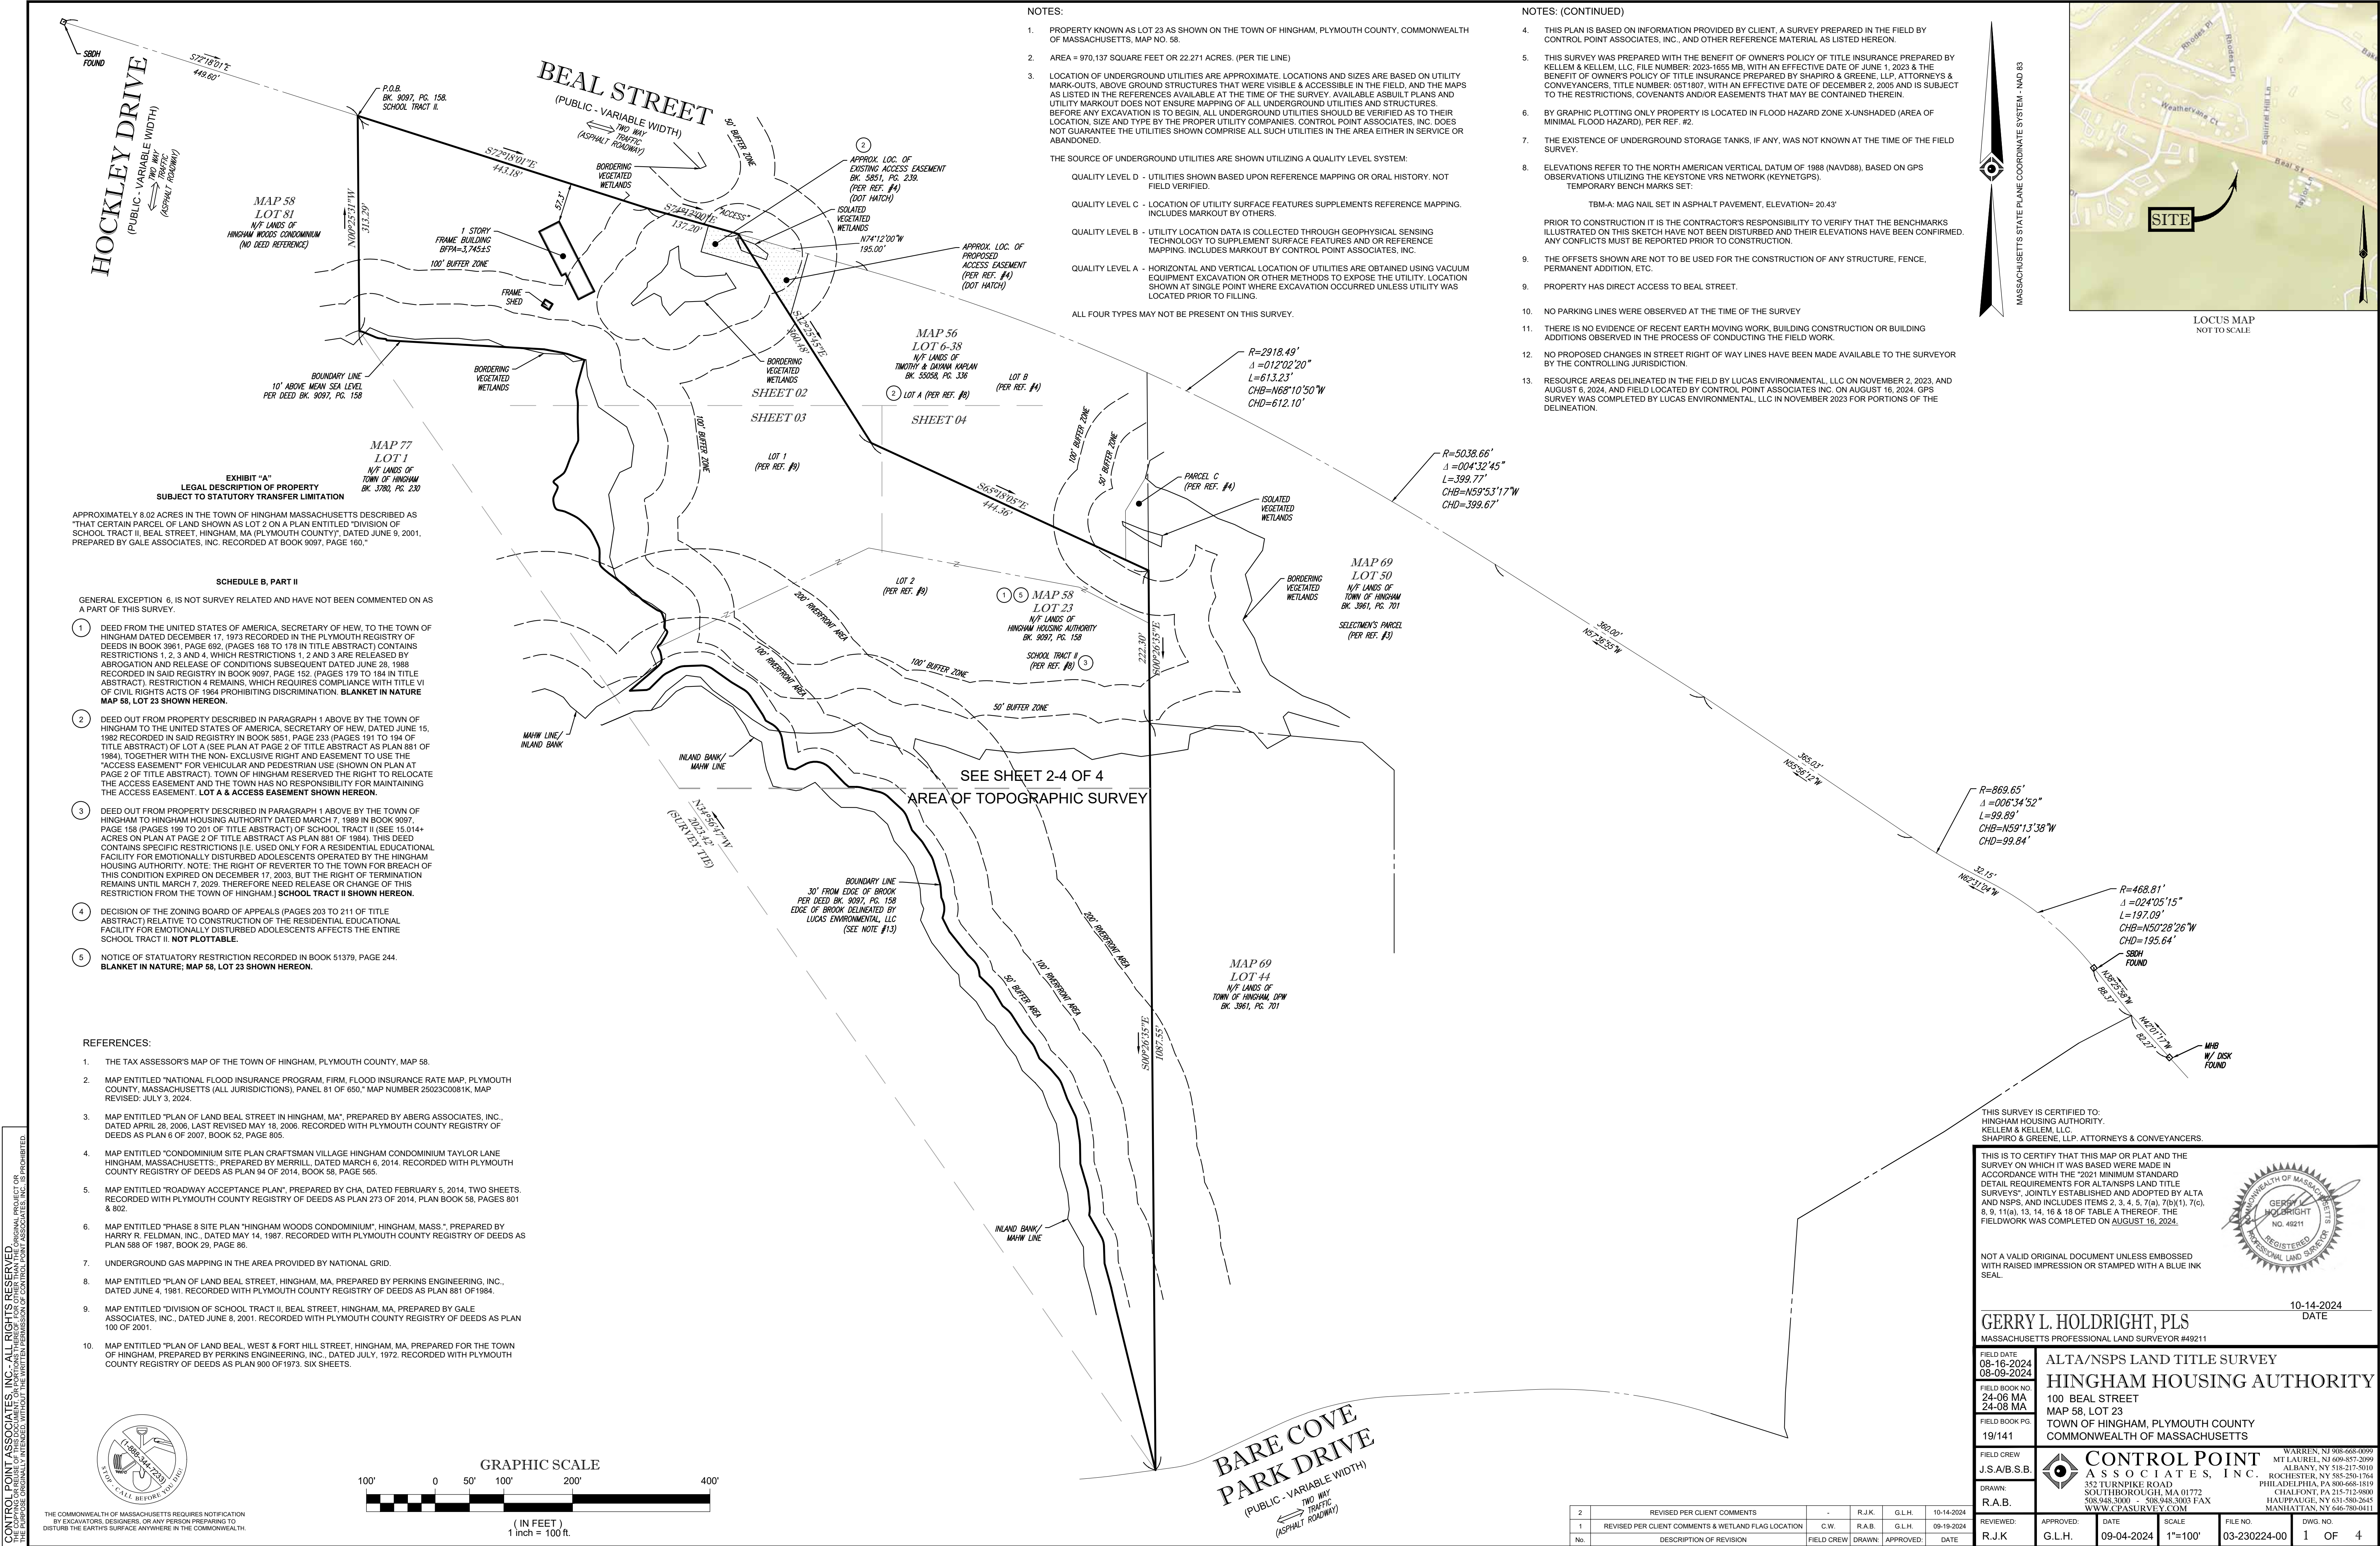





CONTROL POINT ASSOCIATES, INC. ALL RIGHTS RESERVED. NO PORTION OF THIS MAP OR PLAT MAY BE REPRODUCED OR TRANSMITTED IN ANY FORM OR BY ANY MEANS, ELECTRONIC OR MECHANICAL, WITHOUT THE WRITTEN PERMISSION OF CONTROL POINT ASSOCIATES, INC. IS PROHIBITED.



THE COMMONWEALTH OF MASSACHUSETTS REQUIRES NOTIFICATION BY EXCAVATORS, DESIGNERS, OR ANY PERSON PREPARING TO DISTURB THE EARTH'S SURFACE ANYWHERE IN THE COMMONWEALTH.

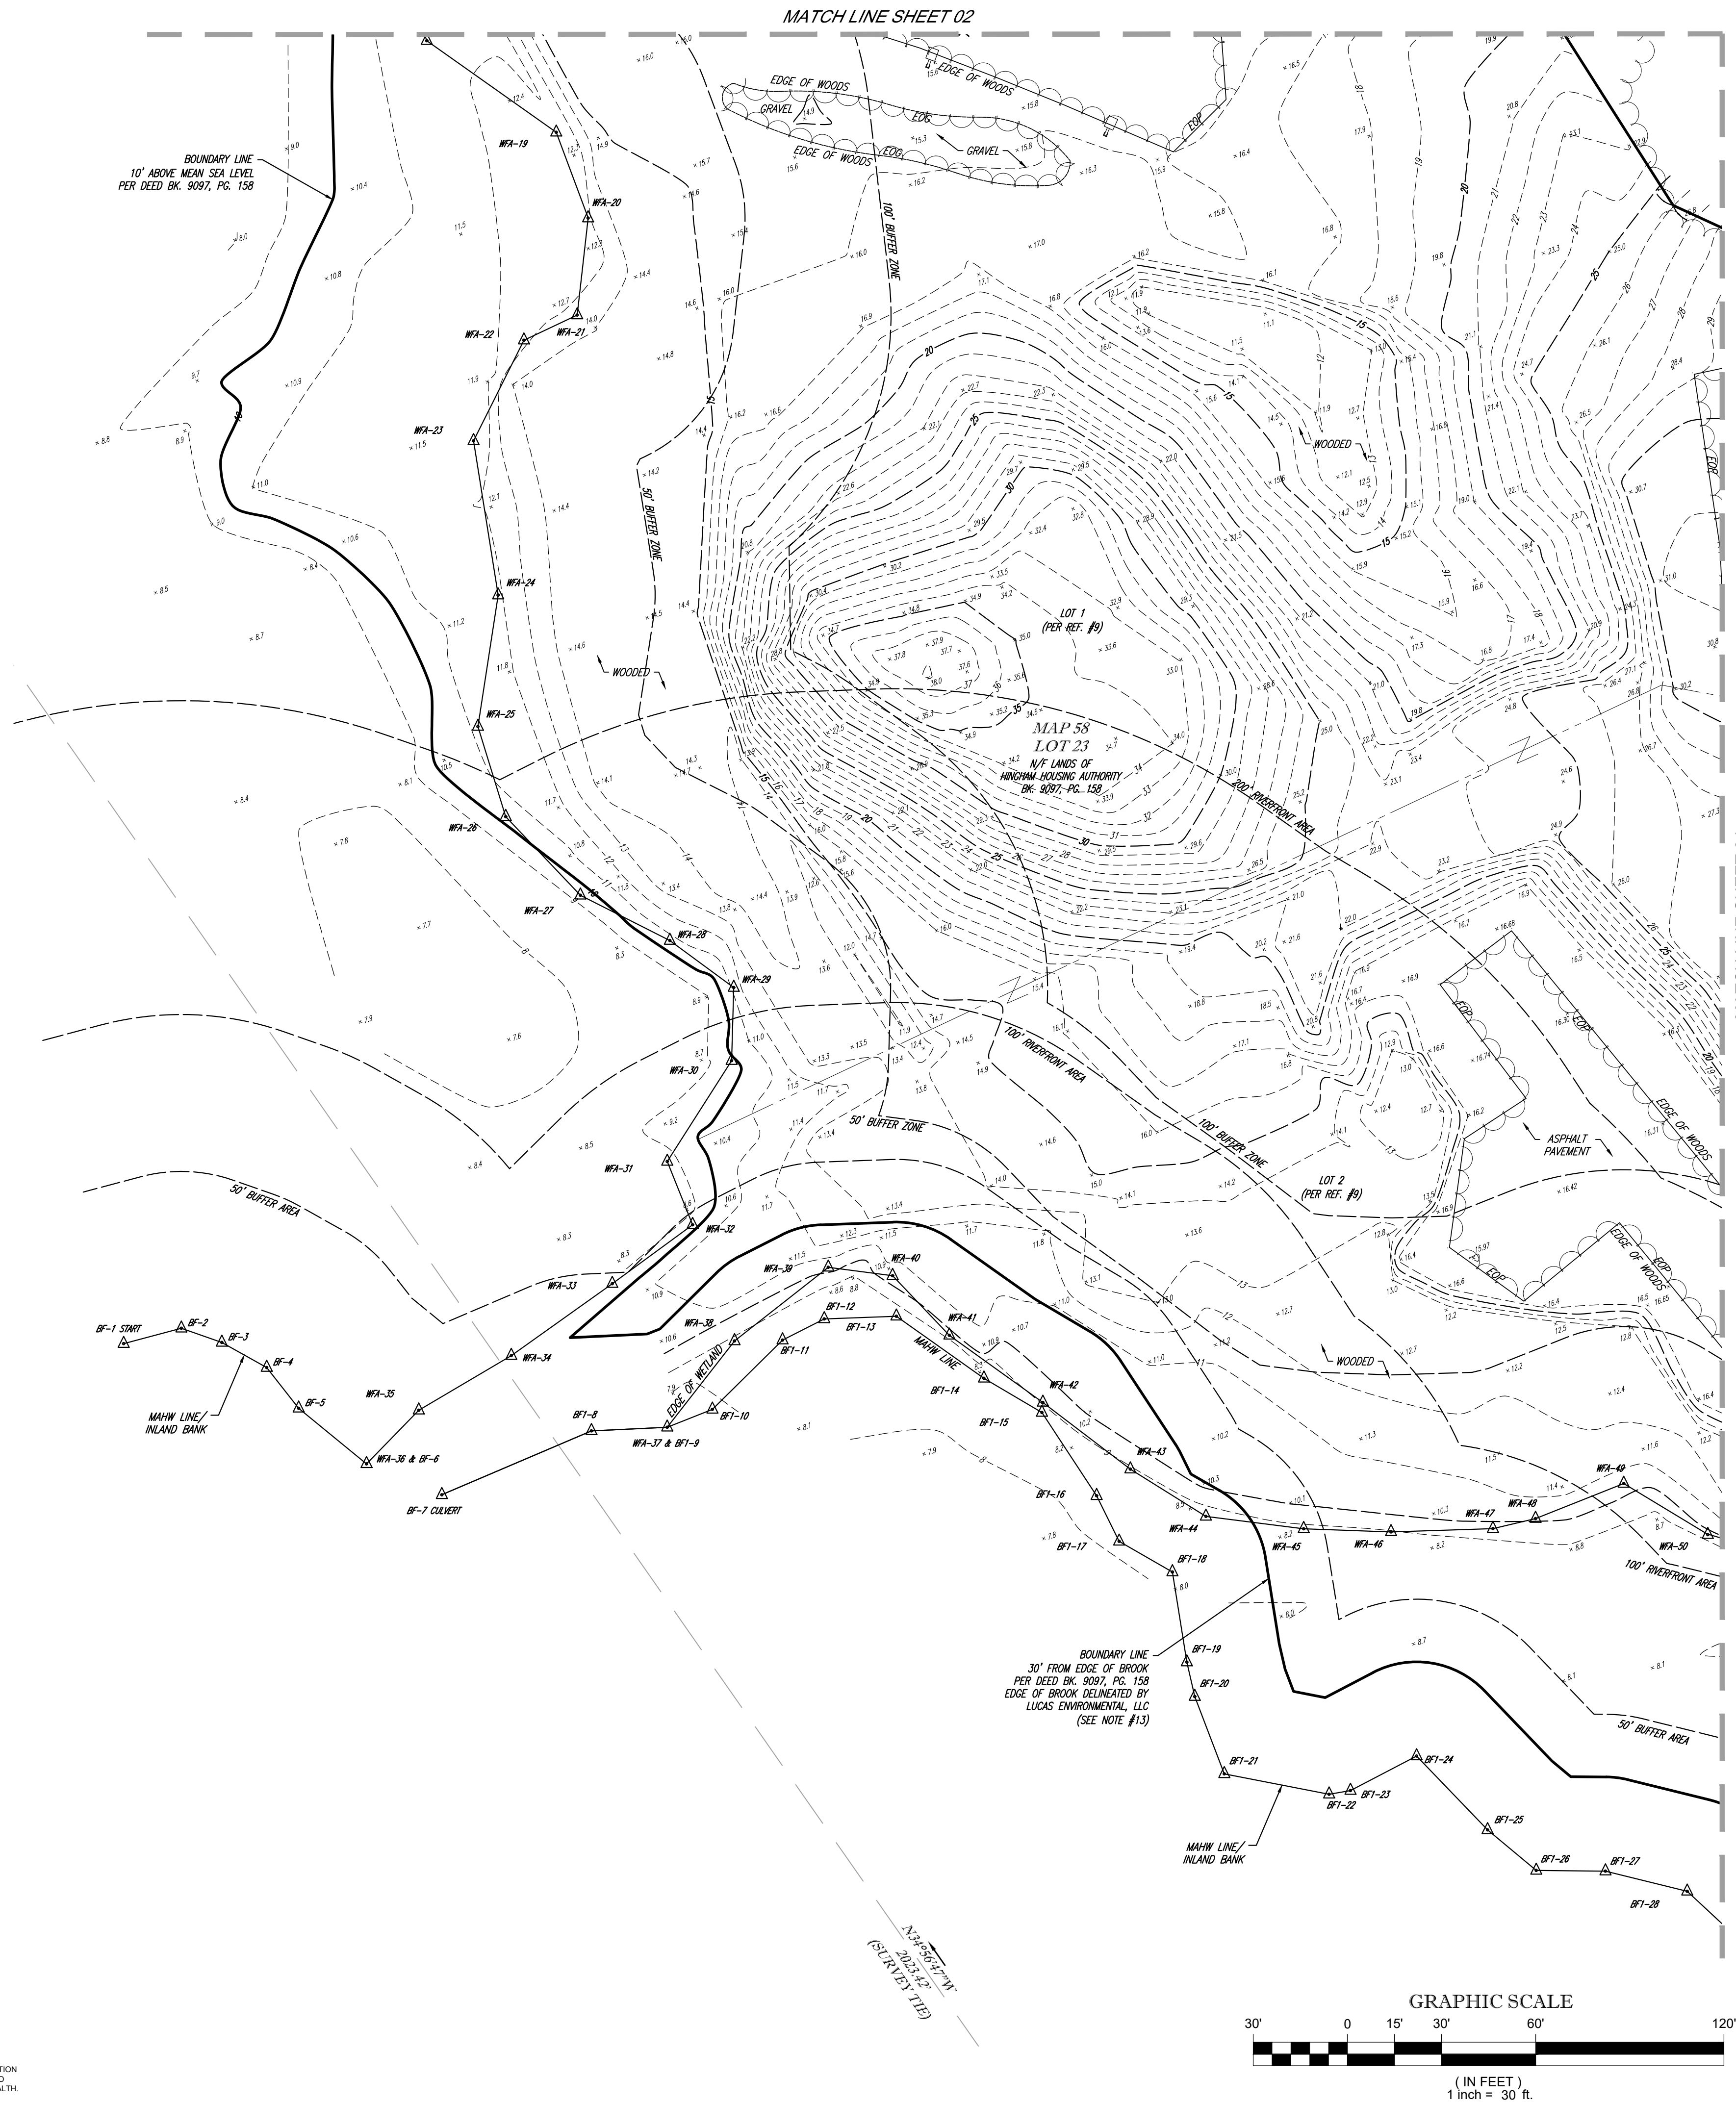

- LEGEND
- 124 --- EXISTING CONTOUR
 - 125 --- EXISTING CONTOUR
 - × 123.45 EXISTING SPOT ELEVATION
 - × TC 123.45 EXISTING TOP OF CURB ELEVATION
 - × BC 123.45 EXISTING TOP OF CURB ELEVATION
 - × TW 123.45 EXISTING TOP OF WALL ELEVATION
 - × BW 122.95 EXISTING BOTTOM OF WALL ELEVATION
 - OH — OVERHEAD WIRES
 - G — APPROX. LOC. UNDERGROUND GAS LINE
 - D — APPROX. LOC. UNDERGROUND DRAINAGE LINE
 - UP /- UTILITY POLE
 - SIGN
 - SMH SANITARY/SEWER MANHOLE
 - DMH DRAINAGE/STORM MANHOLE
 - MH UNKNOWN MANHOLE
 - EOP EDGE OF PAVEMENT
 - CLF CHAIN LINK FENCE
 - LSA LANDSCAPED AREA
 - (TP) TYPICAL
 - EL ELEVATION
 - PVC POLYVINYL CHLORIDE PIPE
 - RCP REINFORCED CONCRETE PIPE
 - INV INVERT ELEVATION
 - GR1 GRATE ELEVATION
 - 1.0' OFFSET OF STRUCTURE AT GROUND LEVEL RELATIVE TO PROPERTY LINE
 - 0.0' SUBSURFACE UTILITY QUALITY LEVEL D

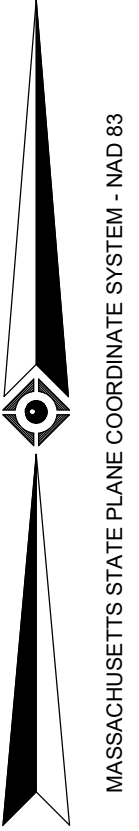

THIS SURVEY IS CERTIFIED TO:
HINGHAM HOUSING AUTHORITY.
KELLEM & KELLEM, LLC.
SHAPIRO & GREENE, LLP, ATTORNEYS & CONVEYANCERS.

THIS IS TO CERTIFY THAT THIS MAP OR PLAT AND THE SURVEY ON WHICH IT WAS BASED WERE MADE IN ACCORDANCE WITH THE "2021 MINIMUM STANDARD DETAIL REQUIREMENTS FOR ALTA/NSPS LAND TITLE SURVEYS", JOINTLY ESTABLISHED AND ADOPTED BY ALTA AND NSPS, AND INCLUDES ITEMS 2, 3, 4, 5, 7(a), 7(b)(1), 7(c), 8, 9, 11(a), 13, 14, 16 & 18 OF TABLE A THEREOF. THE FIELDWORK WAS COMPLETED ON AUGUST 16, 2024.



NOT A VALID ORIGINAL DOCUMENT UNLESS EMBOSSED WITH RAISED IMPRESSION OR STAMPED WITH A BLUE INK SEAL.

GERRY L. HOLDRIGHT, PLS
MASSACHUSETTS PROFESSIONAL LAND SURVEYOR #49211

10-14-2024
DATE

2	REVISED PER CLIENT COMMENTS	-	R.J.K.	G.L.H.	10-14-2024
1	REVISED PER CLIENT COMMENTS & WETLAND FLAG LOCATION	C.W.	R.A.B.	G.L.H.	09-19-2024
No.	DESCRIPTION OF REVISION	FIELD CREW	DRAWN	APPROVED	DATE
FIELD DATE	08-16-2024	ALTA/NSPS LAND TITLE SURVEY			
FIELD BOOK NO.	08-09-2024	HINGHAM HOUSING AUTHORITY			
FIELD BOOK NO.	24-06 MA	100 BEAL STREET			
FIELD BOOK NO.	24-08 MA	MAP 58, LOT 23			
FIELD BOOK PG.	19/141	TOWN OF HINGHAM, PLYMOUTH COUNTY			
FIELD CREW	J.S.A./B.S.B.	COMMONWEALTH OF MASSACHUSETTS			
DRAWN	R.A.B.	CONTROL POINT ASSOCIATES, INC.			
REVIEWED	R.J.K.	APPROVED	G.L.H.	DATE	09-04-2024
SCALE	1"=30'	FILE NO.	03-230224-00	DWG. NO.	3 OF 4

